


voorgevel

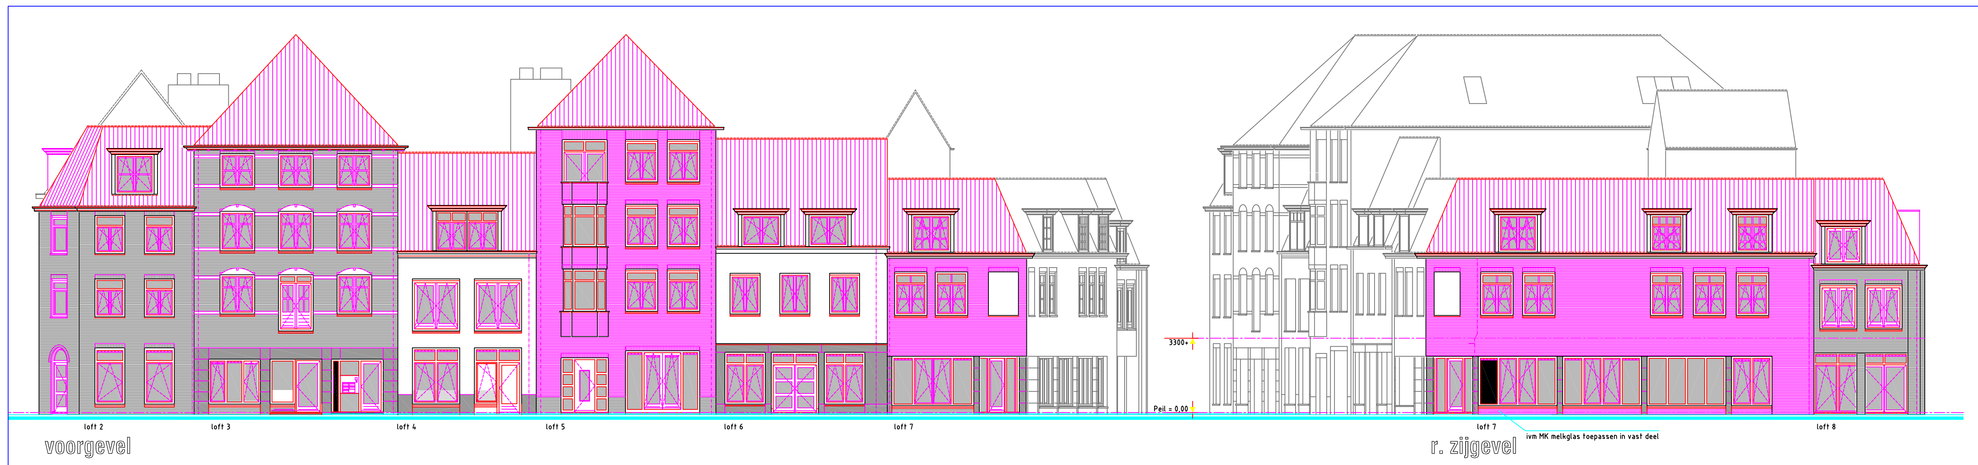


r. zijgevel

achtergevel

l. zijgevel

begane grond

LOFT 1

| nr. | ruimte | ruimtesoort | GBO | VR |
|---|---|---|---|---|
| 0.01 | berging 1 | functieruimte | 20,9 $m^2$ | |
| 0.02 | hal | verkeersruimte | 4,8 $m^2$ | |
| 0.03 | toilet | toiletruimte | 1,3 $m^2$ | |
| 0.04 | badkamer | badruimte | 5,7 $m^2$ | |
| 0.05 | slaapkamer | verblijfsruimte | 16,9 $m^2$ | 16,9 $m^2$ |
| 0.06 | woonkamer/keuken | verblijfsruimte | 43,9 $m^2$ | 43,9 $m^2$ |

LOFT 2

| nr. | ruimte | ruimtesoort | GBO | VR |
|---|---|---|---|---|
| 0.01 | woonkamer/keuken | verblijfsruimte | 52,6 $m^2$ | 52,6 $m^2$ |
| 0.02 | slaapkamer | verblijfsruimte | 20,0 $m^2$ | 20,0 $m^2$ |
| 0.03 | toilet | toiletruimte | 1,5 $m^2$ | |
| 0.04 | badkamer | badruimte | 4,0 $m^2$ | |
| 0.05 | berging | functieruimte | 2,7 $m^2$ | |

LOFT 3

| nr. | ruimte | ruimtesoort | GBO | VR |
|---|---|---|---|---|
| 0.01 | loft | verblijfsruimte | 91,1 $m^2$ | 91,1 $m^2$ |
| 0.02 | berging | functieruimte | 2,7 $m^2$ | |
| 0.03 | toilet | toiletruimte | 1,5 $m^2$ | |
| 0.04 | badkamer | badruimte | 5,0 $m^2$ | |

LOFT 4

| nr. | ruimte | ruimtesoort | GBO | VR |
|---|---|---|---|---|
| 0.01 | loft | verblijfsruimte | 109,9 $m^2$ | 109,9 $m^2$ |
| 0.02 | berging | functieruimte | 2,7 $m^2$ | |
| 0.03 | toilet | toiletruimte | 1,5 $m^2$ | |
| 0.04 | badkamer | badruimte | 5,0 $m^2$ | |

LOFT 5

| nr. | ruimte | ruimtesoort | GBO | VR |
|---|---|---|---|---|
| 0.01 | hal | verkeersruimte | 3,3 $m^2$ | |
| 0.02 | loft | verblijfsruimte | 119,7 $m^2$ | 119,7 $m^2$ |
| 0.03 | berging | functieruimte | 2,7 $m^2$ | |
| 0.04 | toilet | toiletruimte | 1,5 $m^2$ | |
| 0.05 | badkamer | badruimte | 5,0 $m^2$ | |

LOFT 6

| nr. | ruimte | ruimtesoort | GBO | VR |
|---|---|---|---|---|
| 0.01 | hal | verkeersruimte | 3,0 $m^2$ | |
| 0.02 | loft | verblijfsruimte | 106,3 $m^2$ | 106,3 $m^2$ |
| 0.03 | berging | functieruimte | 2,7 $m^2$ | |
| 0.04 | toilet | toiletruimte | 1,5 $m^2$ | |
| 0.05 | badkamer | badruimte | 4,0 $m^2$ | |

LOFT 7

| nr. | ruimte | ruimtesoort | GBO | VR |
|---|---|---|---|---|
| 0.01 | woonkamer/keuken | verblijfsruimte | 61,9 $m^2$ | 61,9 $m^2$ |
| 0.02 | slaapkamer | verblijfsruimte | 19,6 $m^2$ | 19,6 $m^2$ |
| 0.03 | gang | verkeersruimte | 4,7 $m^2$ | |
| 0.04 | berging | functieruimte | 2,7 $m^2$ | |
| 0.05 | toilet | toiletruimte | 1,5 $m^2$ | |
| 0.06 | badkamer | badruimte | 4,0 $m^2$ | |

LOFT 8

| nr. | ruimte | ruimtesoort | GBO | VR |
|---|---|---|---|---|
| 0.01 | hal | verkeersruimte | 6,8 $m^2$ | |
| 0.02 | toilet | toiletruimte | 2,3 $m^2$ | |
| 0.03 | badkamer | badruimte | 5,1 $m^2$ | |
| 0.04 | berging | functieruimte | 4,3 $m^2$ | |
| 0.05 | loft | verblijfsruimte | 60,6 $m^2$ | 60,6 $m^2$ |

MATERIALEN - EN KLEURENSTAAT

| onderdeel | materiaal | kleur |
|---|---|---|
| loft 1 | | |
| kozijnen | h. hout | RAL 6005 |
| deuren | h. hout | RAL 6005 |
| ramen | h. hout | RAL 9010 |
| waterslag | beton | grijs |
| loft 2 t/m 7 en entree | | |
| kozijnen, deuren en ramen | h. hout | RAL 9002 |
| balustrades | staal | RAL 9005 |
| balustrade (loft 4) | hardglas | natuurl. |
| waterslagen (loft 4) | beton | grijs |
| borstwering (loft 4) | stucwerk | anthraciet |
| loft 8 | | |
| kozijnen en ramen | aluminium | RAL 9005 |
| balustrades | staal | RAL 9005 |




ALLE MATEN IN HET WERK TE CONTROLEREN


stan aarts architecten

adresgegevens: Kruisstraat 33, 4561 CB Hoeven, Nederland
Architectenregister nr. 1.020501.001

contactgegevens: T. +31 (0)193 54 42 28, E. info@stanaarts.nl, W. www.stanaarts.com

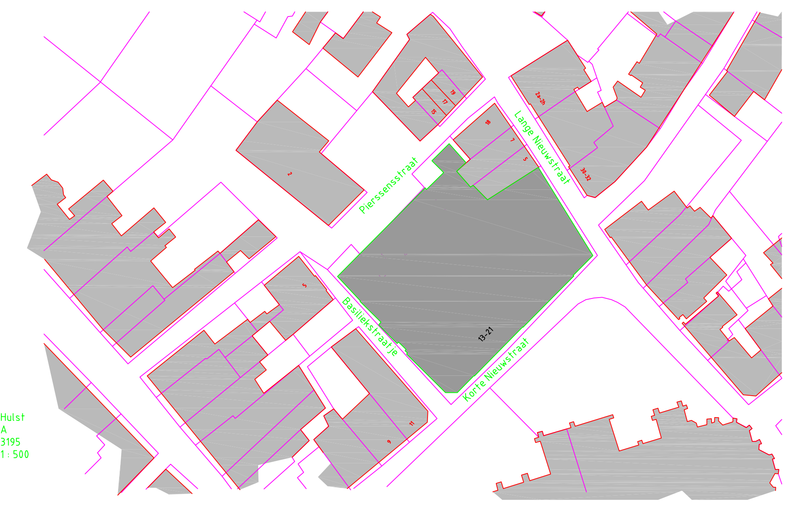bedrijfsgegevens: KVK. 20080703, BTW. NL001.002.962.B01, IBAN. NL20 RABO 0174 3260.61


| | |
|---|---|
| + d. opdrachtgever | Woonstichting Hulst<br>Godsplein 23<br>4561 BD Hulst |
| + project | Herontwikkeling<br>Korte Nieuwstraat 13-21<br>te Hulst |
| + onderdeel | FASE DO<br>situatie, plattegrond en gevels nieuw |
| + adres | - |
| + projectnummer | 021-068 |
| + gem. ref. nr. | - |
| + bladnummer | VO.02.a |
| + wijzigingsdatum | a. 19-01-2022<br>b. 23-09-2025<br>c. 24-11-2025<br>d. 14-01-2026<br>e. 22-01-2026 |
| + datum | 18-01-2022 |
| + getekend | R.v. |
| + schaal | 1:500/100 |
| + afmeting | A0+ |