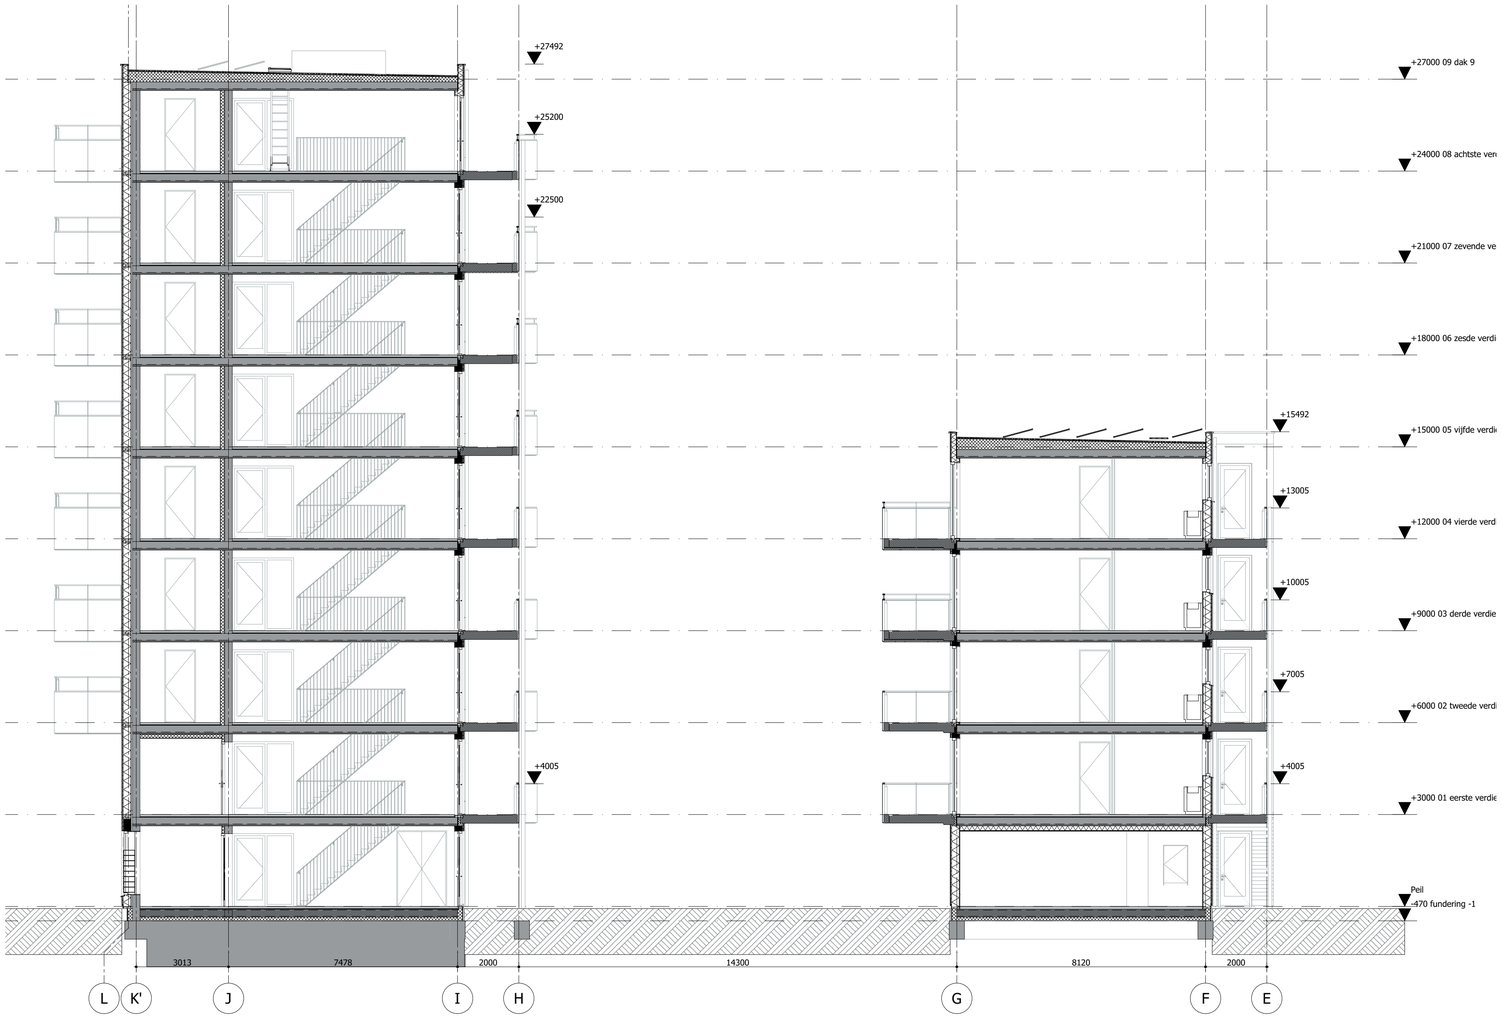

PLEGT-VOS

Ingekomen	W.V.B. d.d.	22-10-2024
Akkoord	W.V.B. d.d.	21-11-2024

Verzonden aan: Zie documentenlijst
Verzonden aan:

DEFINITIEF
PLEGT-VOS

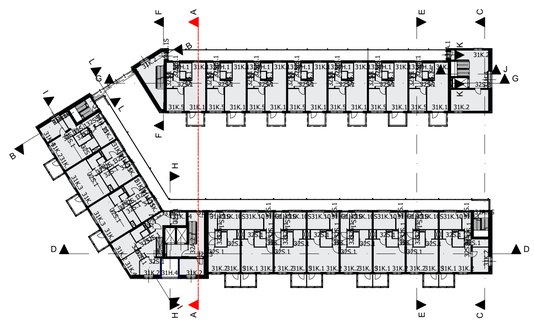

Wijzigingen		
E	Datum	22-10-2024
D	Schaal / formaat	A1 1:100
C	Getekend	P.S. | T.G
B	Opdrachtgever	Havensteder
A		Rotterdam

Tekeningnummer TO.3.01

Projectnummer 210091

Status TO

Fase TO

Doorsnede A-A

Fascinatio Capelle |Capelle aan den IJssel

Blok B1

KAW www.kaw.nl info@kaw.nl +31 88 529 0000 ROTTERDAM Pelgrimsstraat 1 | 3029 BH Rotterdam