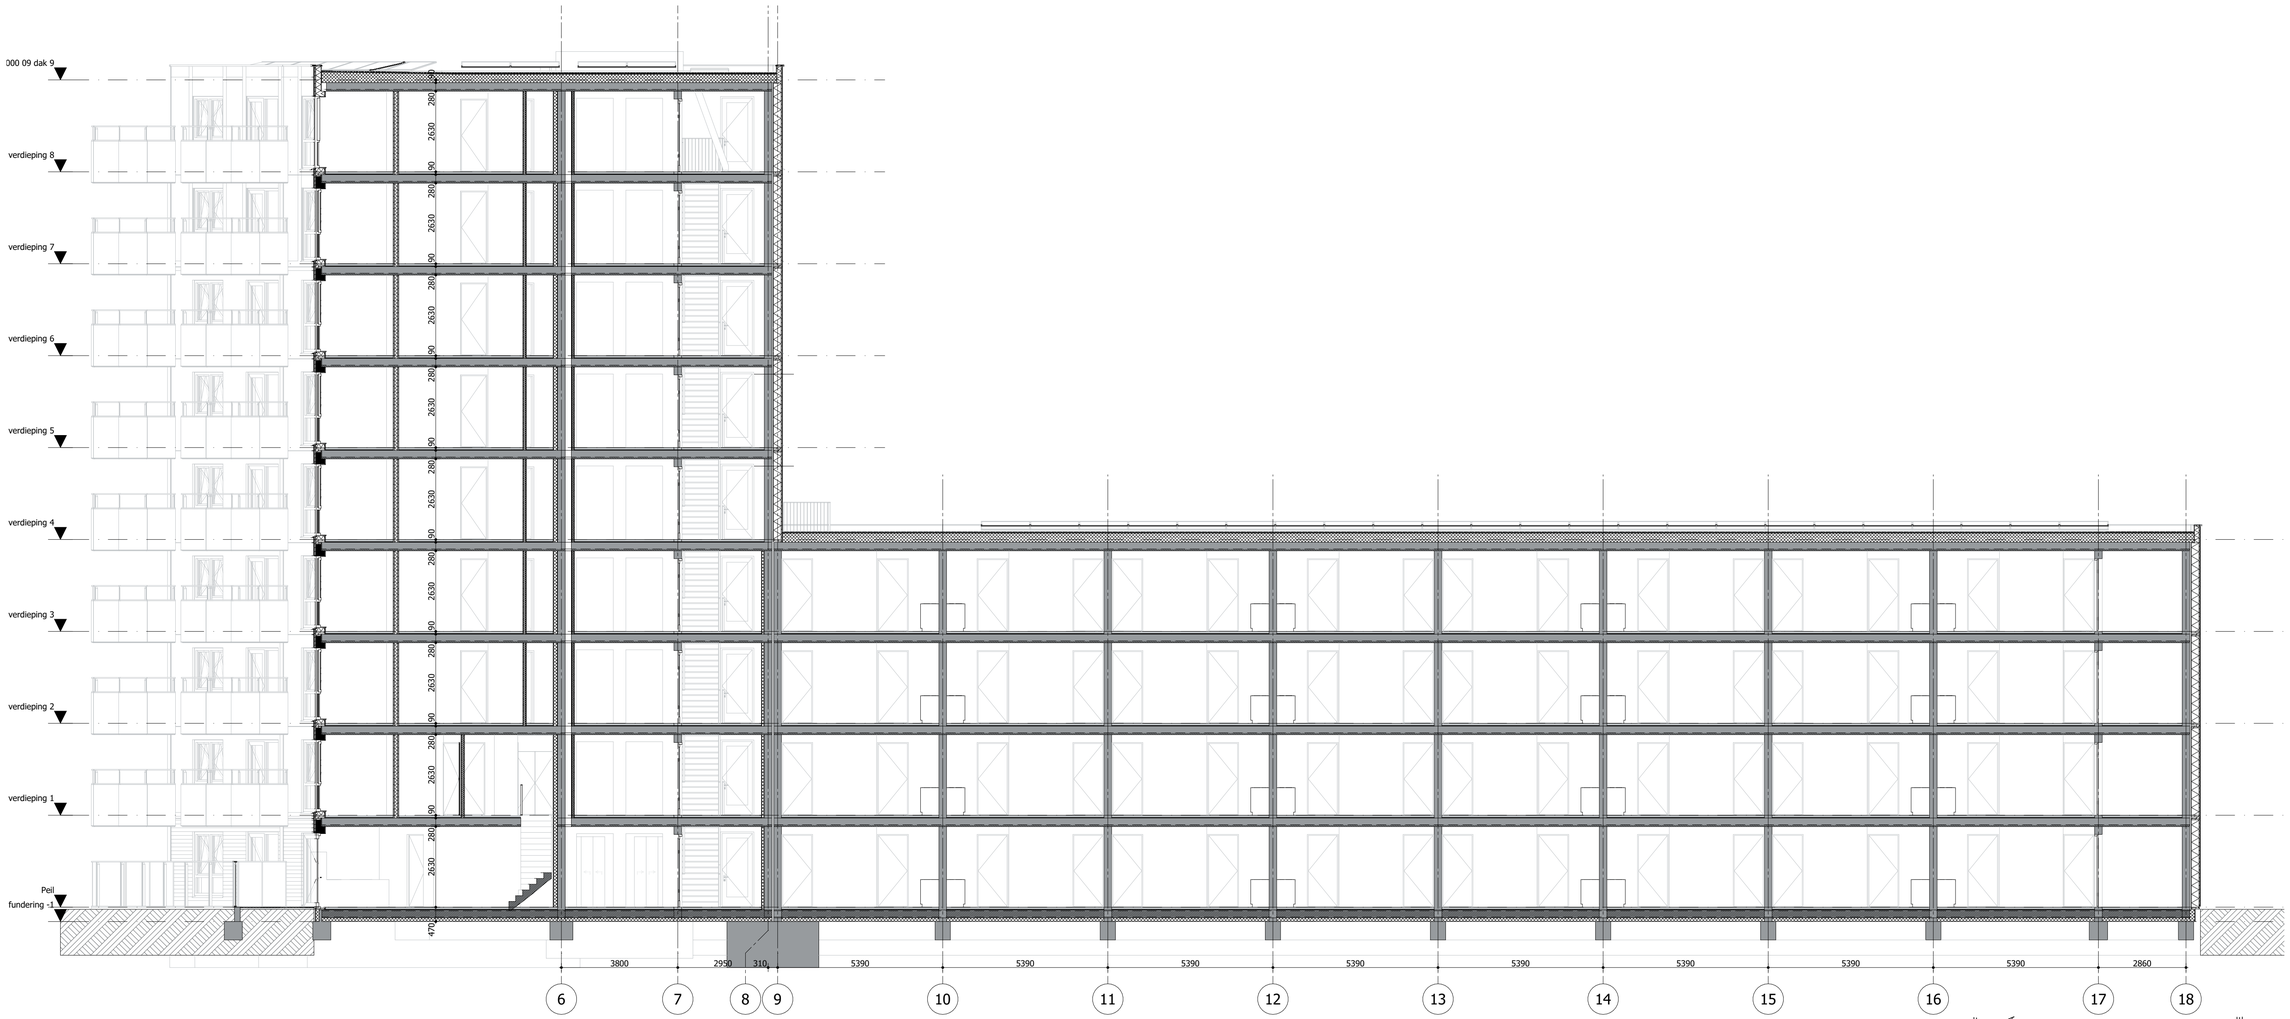

Doorsnede D-D

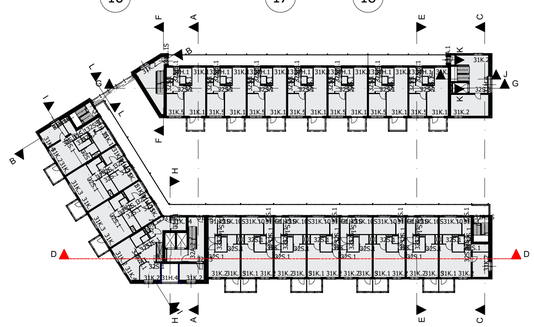

PLEGT-VOS		
Ingekomen	W.V.B. d.d.	22-10-2024
Akkoord	W.V.B. d.d.	21-11-2024
Verzonden aan: Zie documentenlijst		
Verzonden aan:		

DEFINITIEF PLEGT-VOS

Wijzigingen				
E	Datum	22-10-2024	Tekeningnummer	Projectnummer
D	Schaal / formaat	A1 1:100	TO.3.03	210091
C	Getekend	P.S. | T.G	Status	Fase
B	Opdrachtgever	Havensteder Rotterdam	TO	TO
A			Blok B1	

Doorsnede D-D

Fascinatio Capelle \|Capelle aan den IJssel

KAW www.kaw.nl info@kaw.nl +31 88 529 0000 ROTTERDAM Pelgrimsstraat 1 | 3029 BH Rotterdam