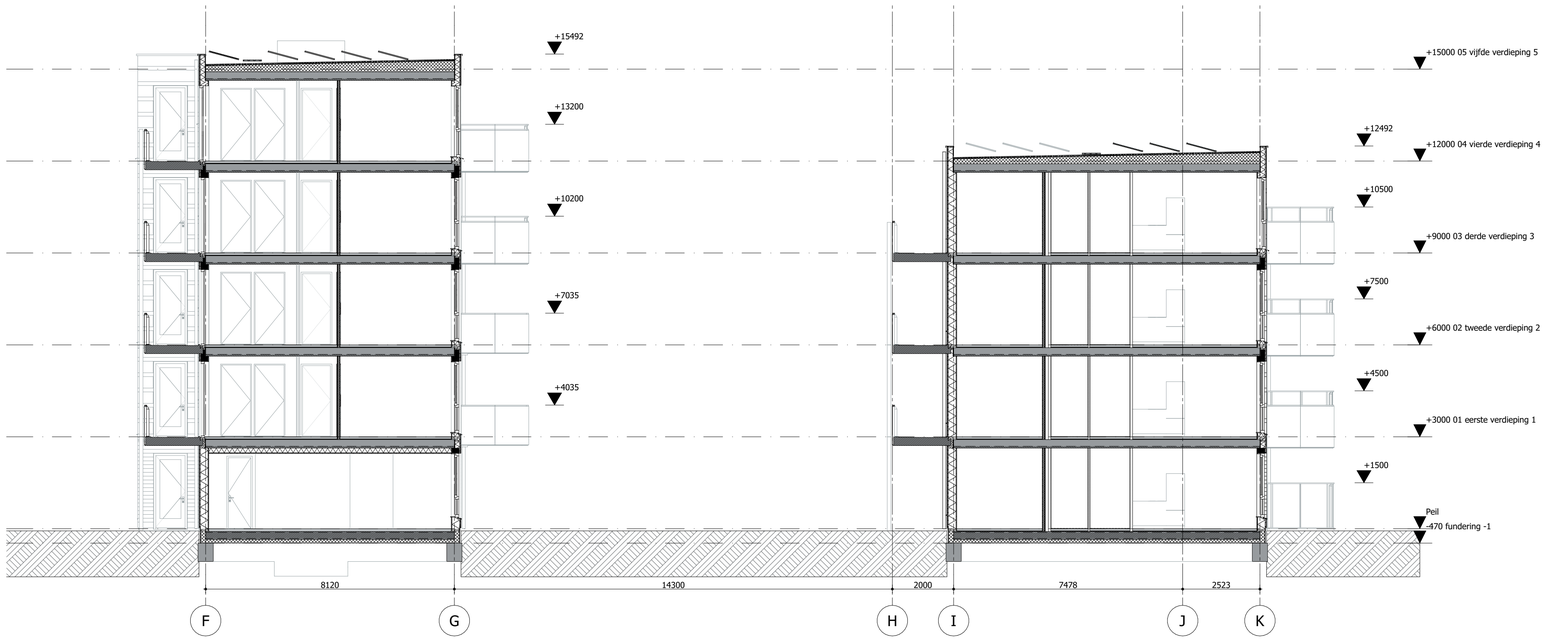


## Doorsnede E-E

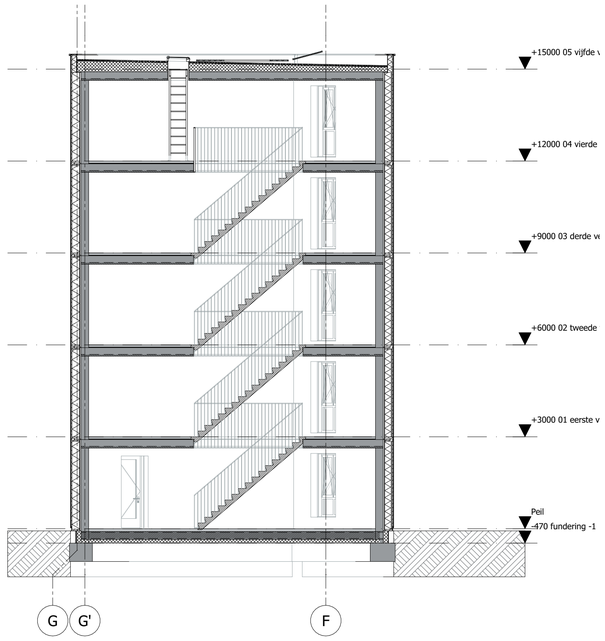


## Doorsnede F-F

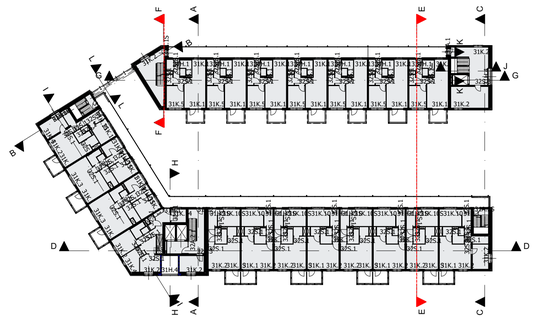

PLEGT-VOS

| | | |
|---|---|---|
| Ingekomen | WVB. d.d. | 22-10-2024 |
| Akkoord | WVB. d.d. | 21-11-2024 |
| Verzonden aan: Zie documentenlijst | | |
| Verzonden aan: | | |

DEFINITIEF
PLEGT-VOS

| Wijzigingen | | | | |
|---|---|---|---|---|
| | Datum | 22-10-2024 | Tekeningnummer | Projectnummer |
| E | Schaal / formaat | A1 1:100 | TO.3.04 | 210091 |
| D | Getekend | P.S. \| T.G | Status | Fase |
| C | Opdrachtgever | Havensteder | TO | TO |
| B | | Rotterdam | | |
| A | | | | |

# Doorsnede E-E, F-F

## Fascinatio Capelle |Capelle aan den IJssel

Blok B1

**KAW** www.kaw.nl info@kaw.nl +31 88 529 0000 ROTTERDAM Pelgrimsstraat 1 | 3029 BH Rotterdam