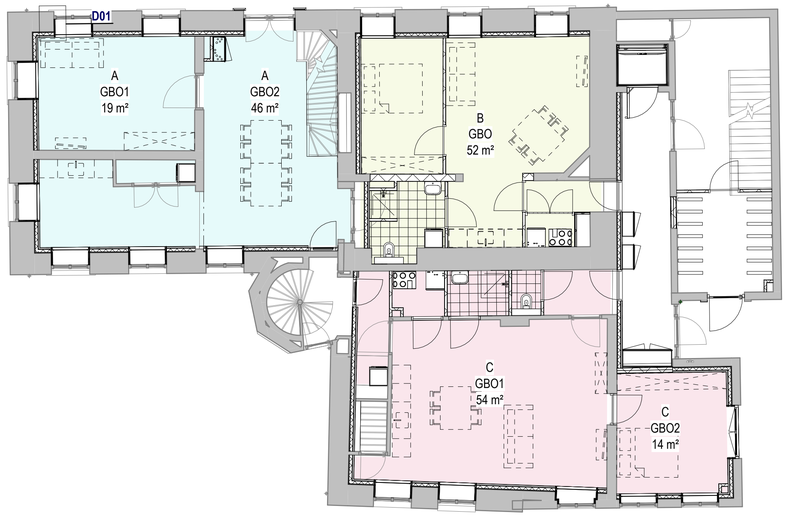

21 - Toetsing - Gebruiksoppervlaktes

- A
- B
- C

00_Begane grondvloer

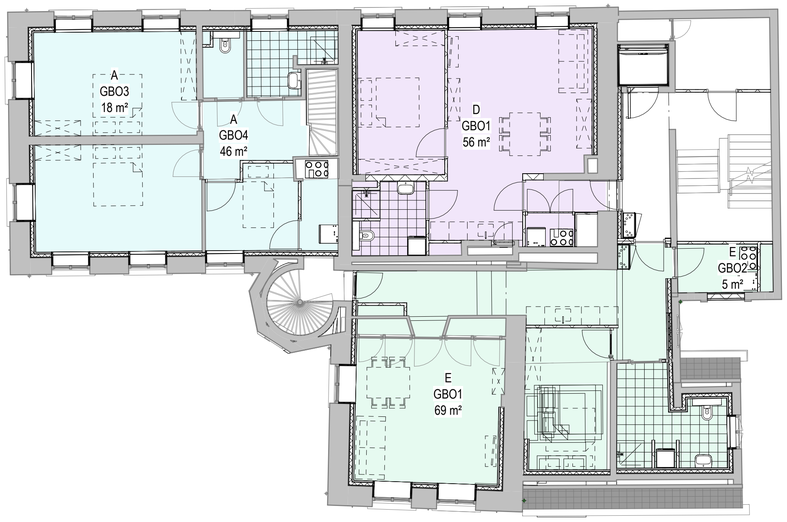

21 - Toetsing - Gebruiksoppervlaktes

- A
- D
- E

1e Verdieping

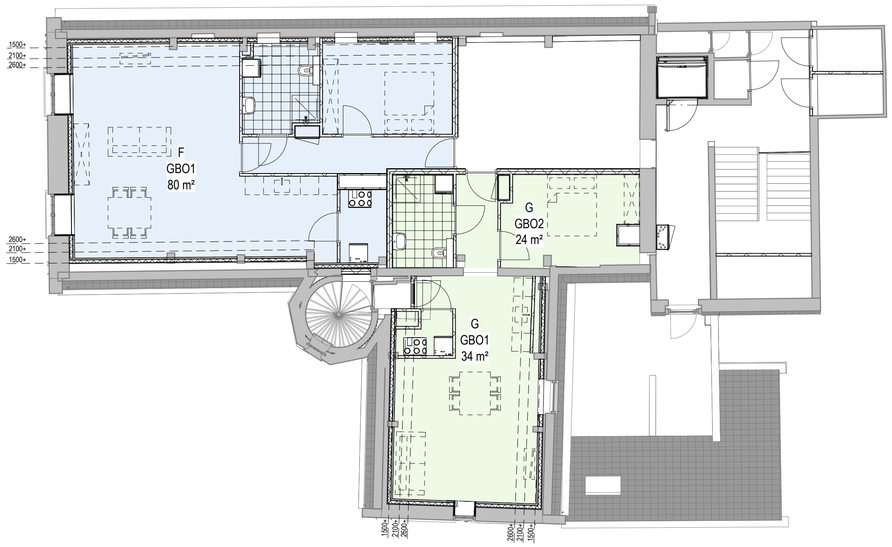

21 - Toetsing - Gebruiksoppervlaktes

- F
- G

2e Verdieping

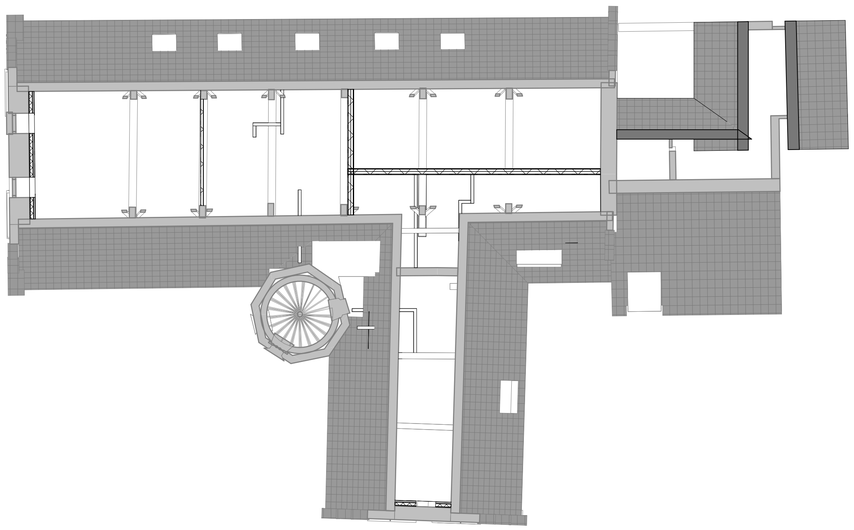

Zolder

Gebruiksoppervlakte

Huisletter	GBO	Oppervlakte
A	GBO1	19 m²
A	GBO2	46 m²
A	GBO3	18 m²
A	GBO4	46 m²
Totaal GBO		129 m²
B	GBO	52 m²
Totaal GBO		52 m²
C	GBO1	54 m²
C	GBO2	14 m²
Totaal GBO		68 m²
D	GBO1	56 m²
Totaal GBO		56 m²

Gebruiksoppervlakte

Huisletter	GBO	Oppervlakte
E	GBO1	69 m²
E	GBO2	5 m²
Totaal GBO		74 m²
F	GBO1	80 m²
		80 m²
Totaal GBO		
G	GBO1	34 m²
G	GBO2	24 m²
		58 m²
Totaal GBO		

VGarchitecten

Architectuur

Oostkade 31 4551 CM Sas van Gent
t+31(0)115 461 41 51 info@VGarchitecten.nl
www.VGarchitecten.nl

Project : Herbestemming Refugium Baudeloo
Adres : Baudeloo 20, 4561ES, Hulst
Opdrachtgever : Woonstichting Hulst

Fase : Aanvraag omgevingsvergunning
Betreft : GBO

Schaal : 1 : 100
Formaat : A1

Revisie	Datum	Getekend	Gezien
0	21-03-2025	RBR	MB

Documentnummer : 2024 013A_DO_11-00